Parcel Table		
SALES LOT	AREA SF	AREA AC
1	6259	0.14
2	6650	0.15
3	5994	0.14
4	5957	0.14
5	5957	0.14
6	5954	0.14
7	5954	0.14
8	5987	0.14
9	5988	0.14
10	5958	0.14
11	5958	0.14
12	5933	0.14
13	5920	0.14
14	5956	0.14
15	5267	0.12
16	5958	0.14
17	4922	0.11
18	4290	0.10
19	4180	0.10
20	4158	0.10
21	4039	0.09
22	4622	0.11
23	13330	0.31
24	11919	0.27
25	15276	0.35
26	13885	0.32
27	12652	0.29
28	12407	0.28
29	12655	0.29
30	12283	0.28

Parcel Table		
SALES LOT	AREA SF	AREA AC
31	12655	0.29
32	12213	0.28
33	12655	0.29
34	12154	0.28
35	12626	0.29
36	12094	0.28
37	10413	0.24
38	12035	0.28
39	9606	0.22
40	11822	0.27
41	14804	0.34
42	26331	0.60
43	19291	0.44
44	9144	0.21
45	11496	0.26
46	11625	0.27
47	15125	0.35
48	11109	0.26
49	24987	0.57
50	11823	0.27
51	12556	0.29
52	16725	0.38
53	13531	0.31
54	13440	0.31
55	21089	0.48
56	12641	0.29
57	12727	0.29
58	12812	0.29
59	13652	0.31
60	16083	0.37

Parcel Table		
SALES LOT	AREA SF	AREA AC
61	20003	0.46
62	18108	0.42
63	16085	0.37
64	16844	0.39
65	14830	0.34
66	14166	0.33
67	19939	0.46
68	39846	0.91
69	25559	0.59
70	13644	0.31
71	11035	0.25
72	11291	0.26
73	11533	0.26
74	11199	0.26
75	11154	0.26
76	11108	0.26
77	14256	0.33
78	13490	0.31
79	11023	0.25
80	9388	0.22
81	10842	0.25
82	18102	0.42
83	16353	0.38
84	28052	0.64

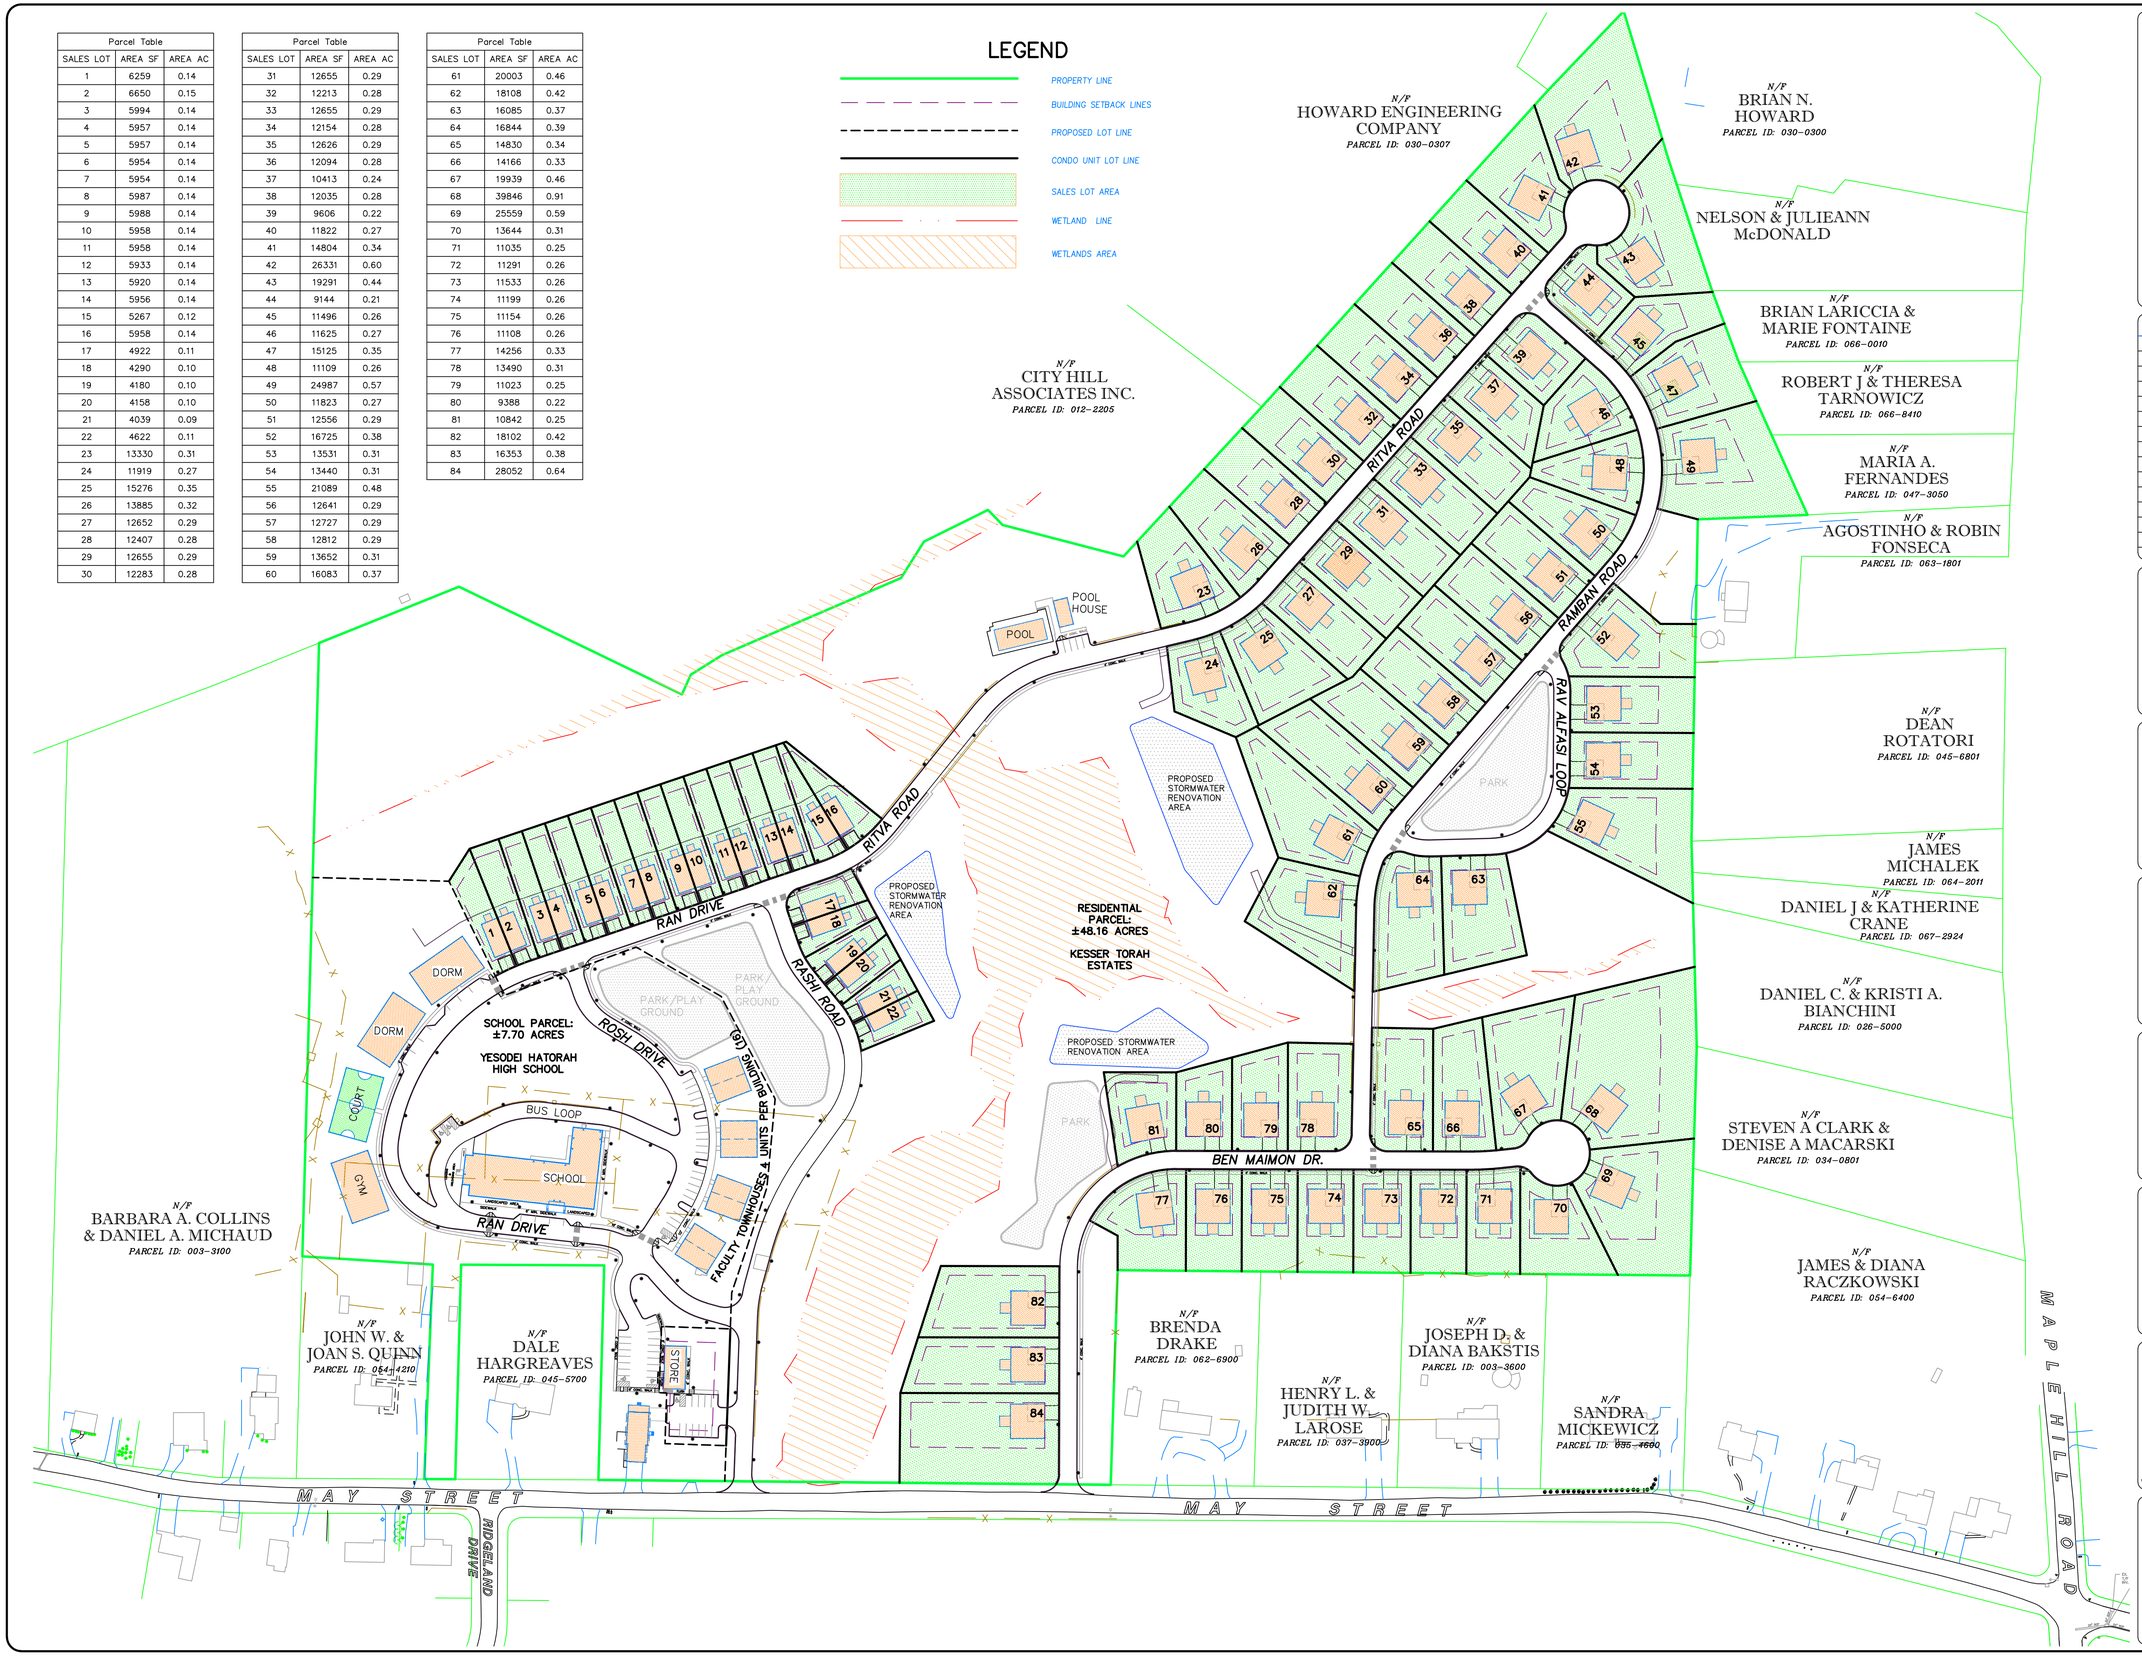

NO.	REVISION	DATE
1	REVISED PER PLANNING COMMENTS	17 JAN 17
2	REV. PER ZONING & ENGINEERING	2 FEB 17
3	REV. PER PLANNING, ZONING, WPCA	27 FEB 17
4	REV. PER CONDITIONS OF APPROVAL	13 APR 17

Previous Editions Obsolete

100 0 50 100 200

1 inch = 100 ft.

YESHIVAS OHR HACHAIM
500 7th AVENUE, 4th FLOOR
NEW YORK, NY

UNIT LAYOUT MAP

YESODEI HATORAH HIGH SCHOOL
&
KESSER TORAH ESTATES

874 MAY STREET

NAUGATUCK CONNECTICUT

CIVIL 1
CORNERSTONE PROFESSIONAL PARK, SUITE D-101
43 SHERMAN HILL ROAD
WOODBURY (203) 266-0778 CONNECTICUT

STATE OF CONNECTICUT CHRISTIS JONES No. 17206 LICENSED PROFESSIONAL ENGINEER

DRAWN: BB	APPROVED: CJ
SCALE:	1" = 100'
DATE:	30 SEP 16
PROJ. NO.:	3405
CADD FILE NAME:	3405
DRAWING NO.:	C - 2.2